
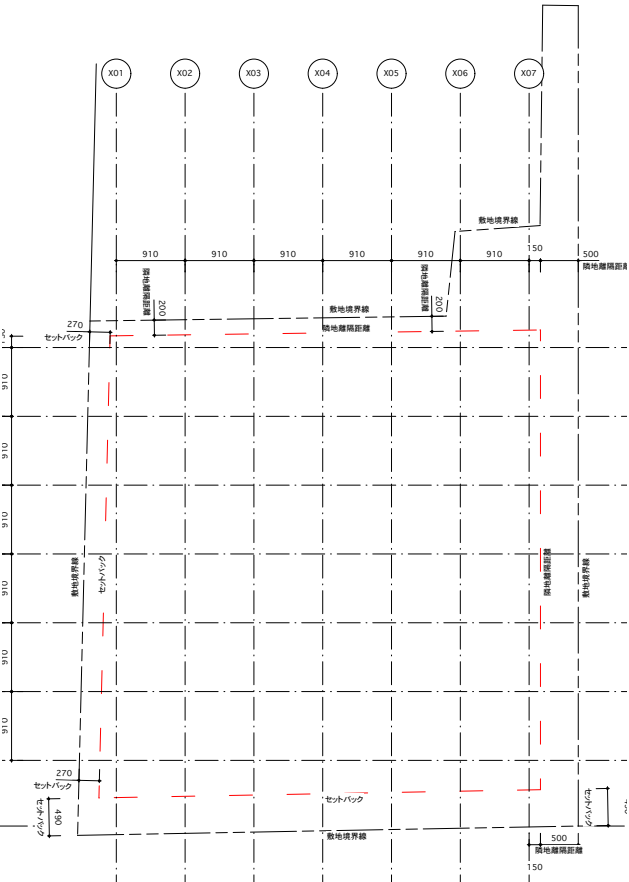
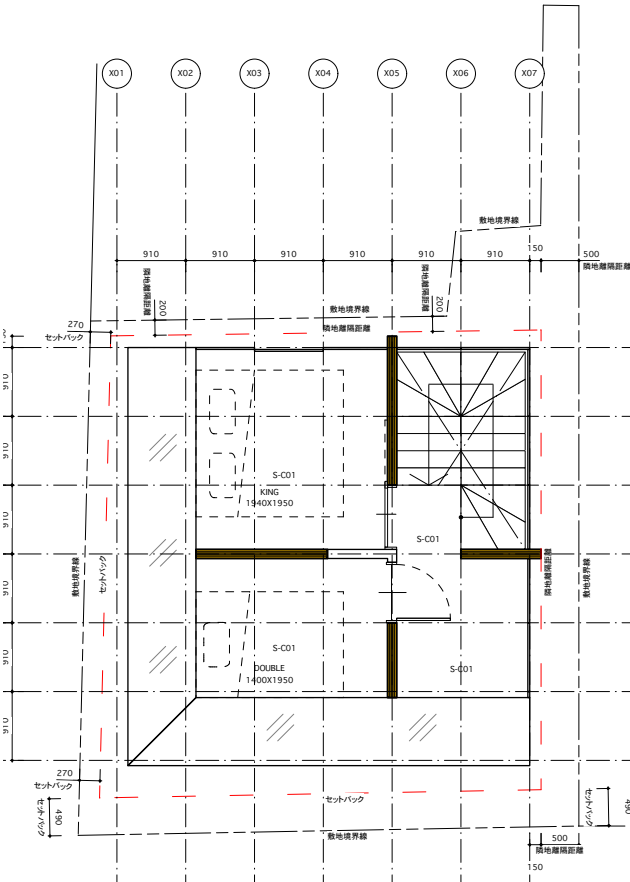
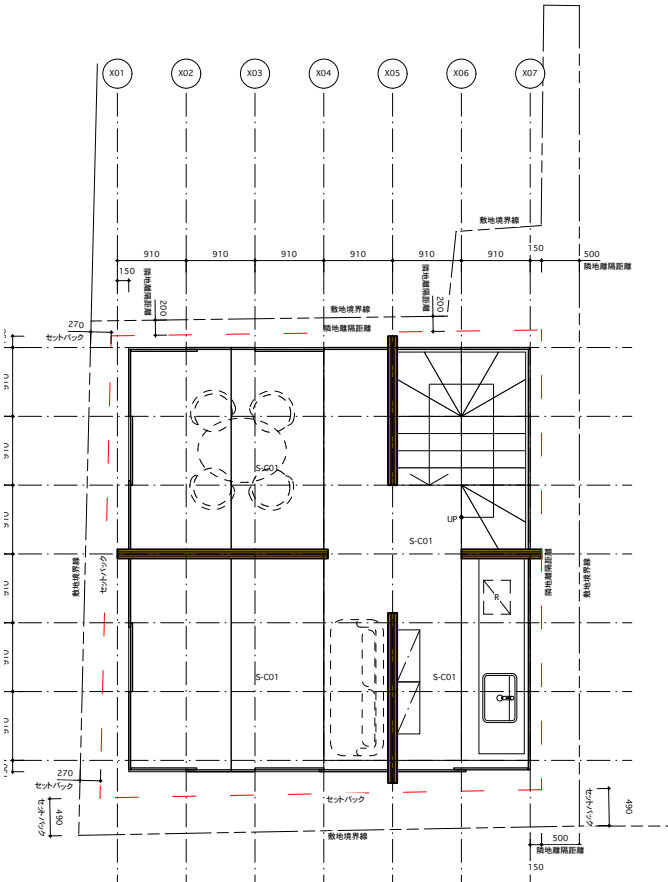


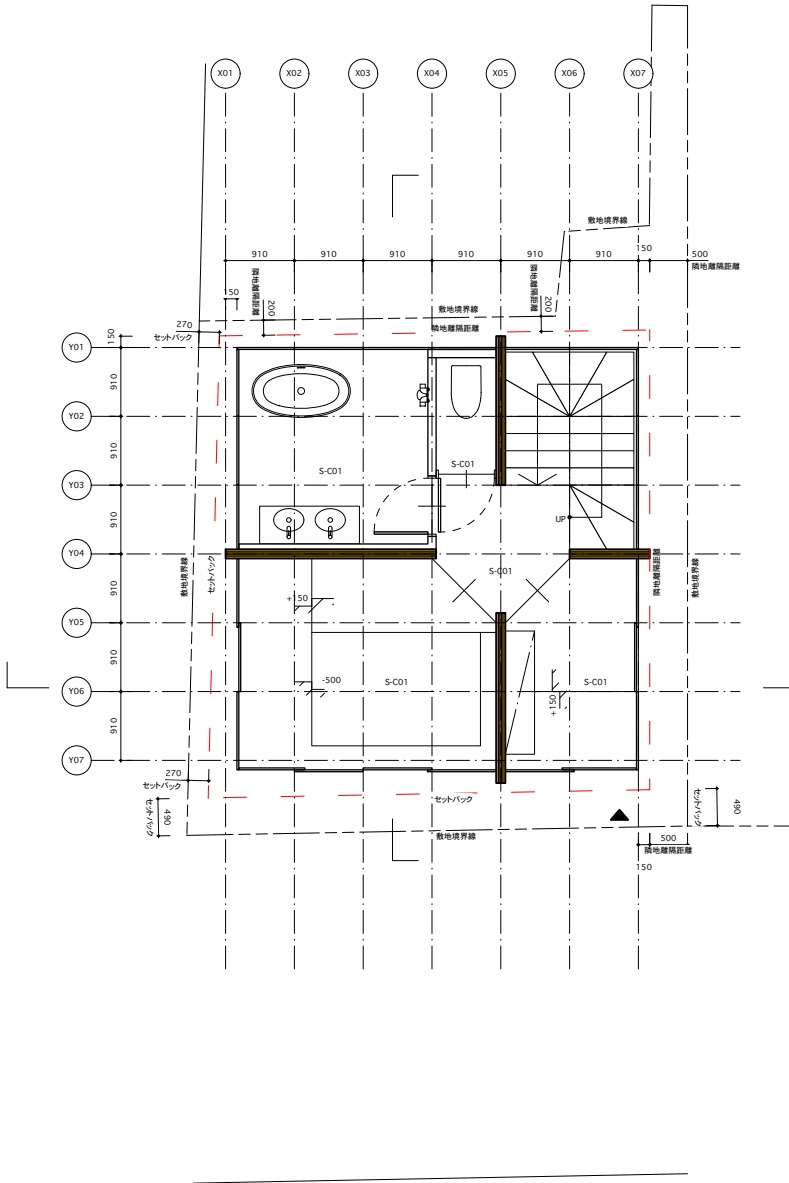


staple studio

〒103-0024
東京都中央区日本橋小舟町14-7
SOIL Nihonbashi 402

第369584号
管理建築士 / 一級建築士
黒木涼

凡例

title	1f~rf平面	scale	1:100	drawn by	no. a-01
project	(仮) hyotan	date	2026/04/21	checked by	

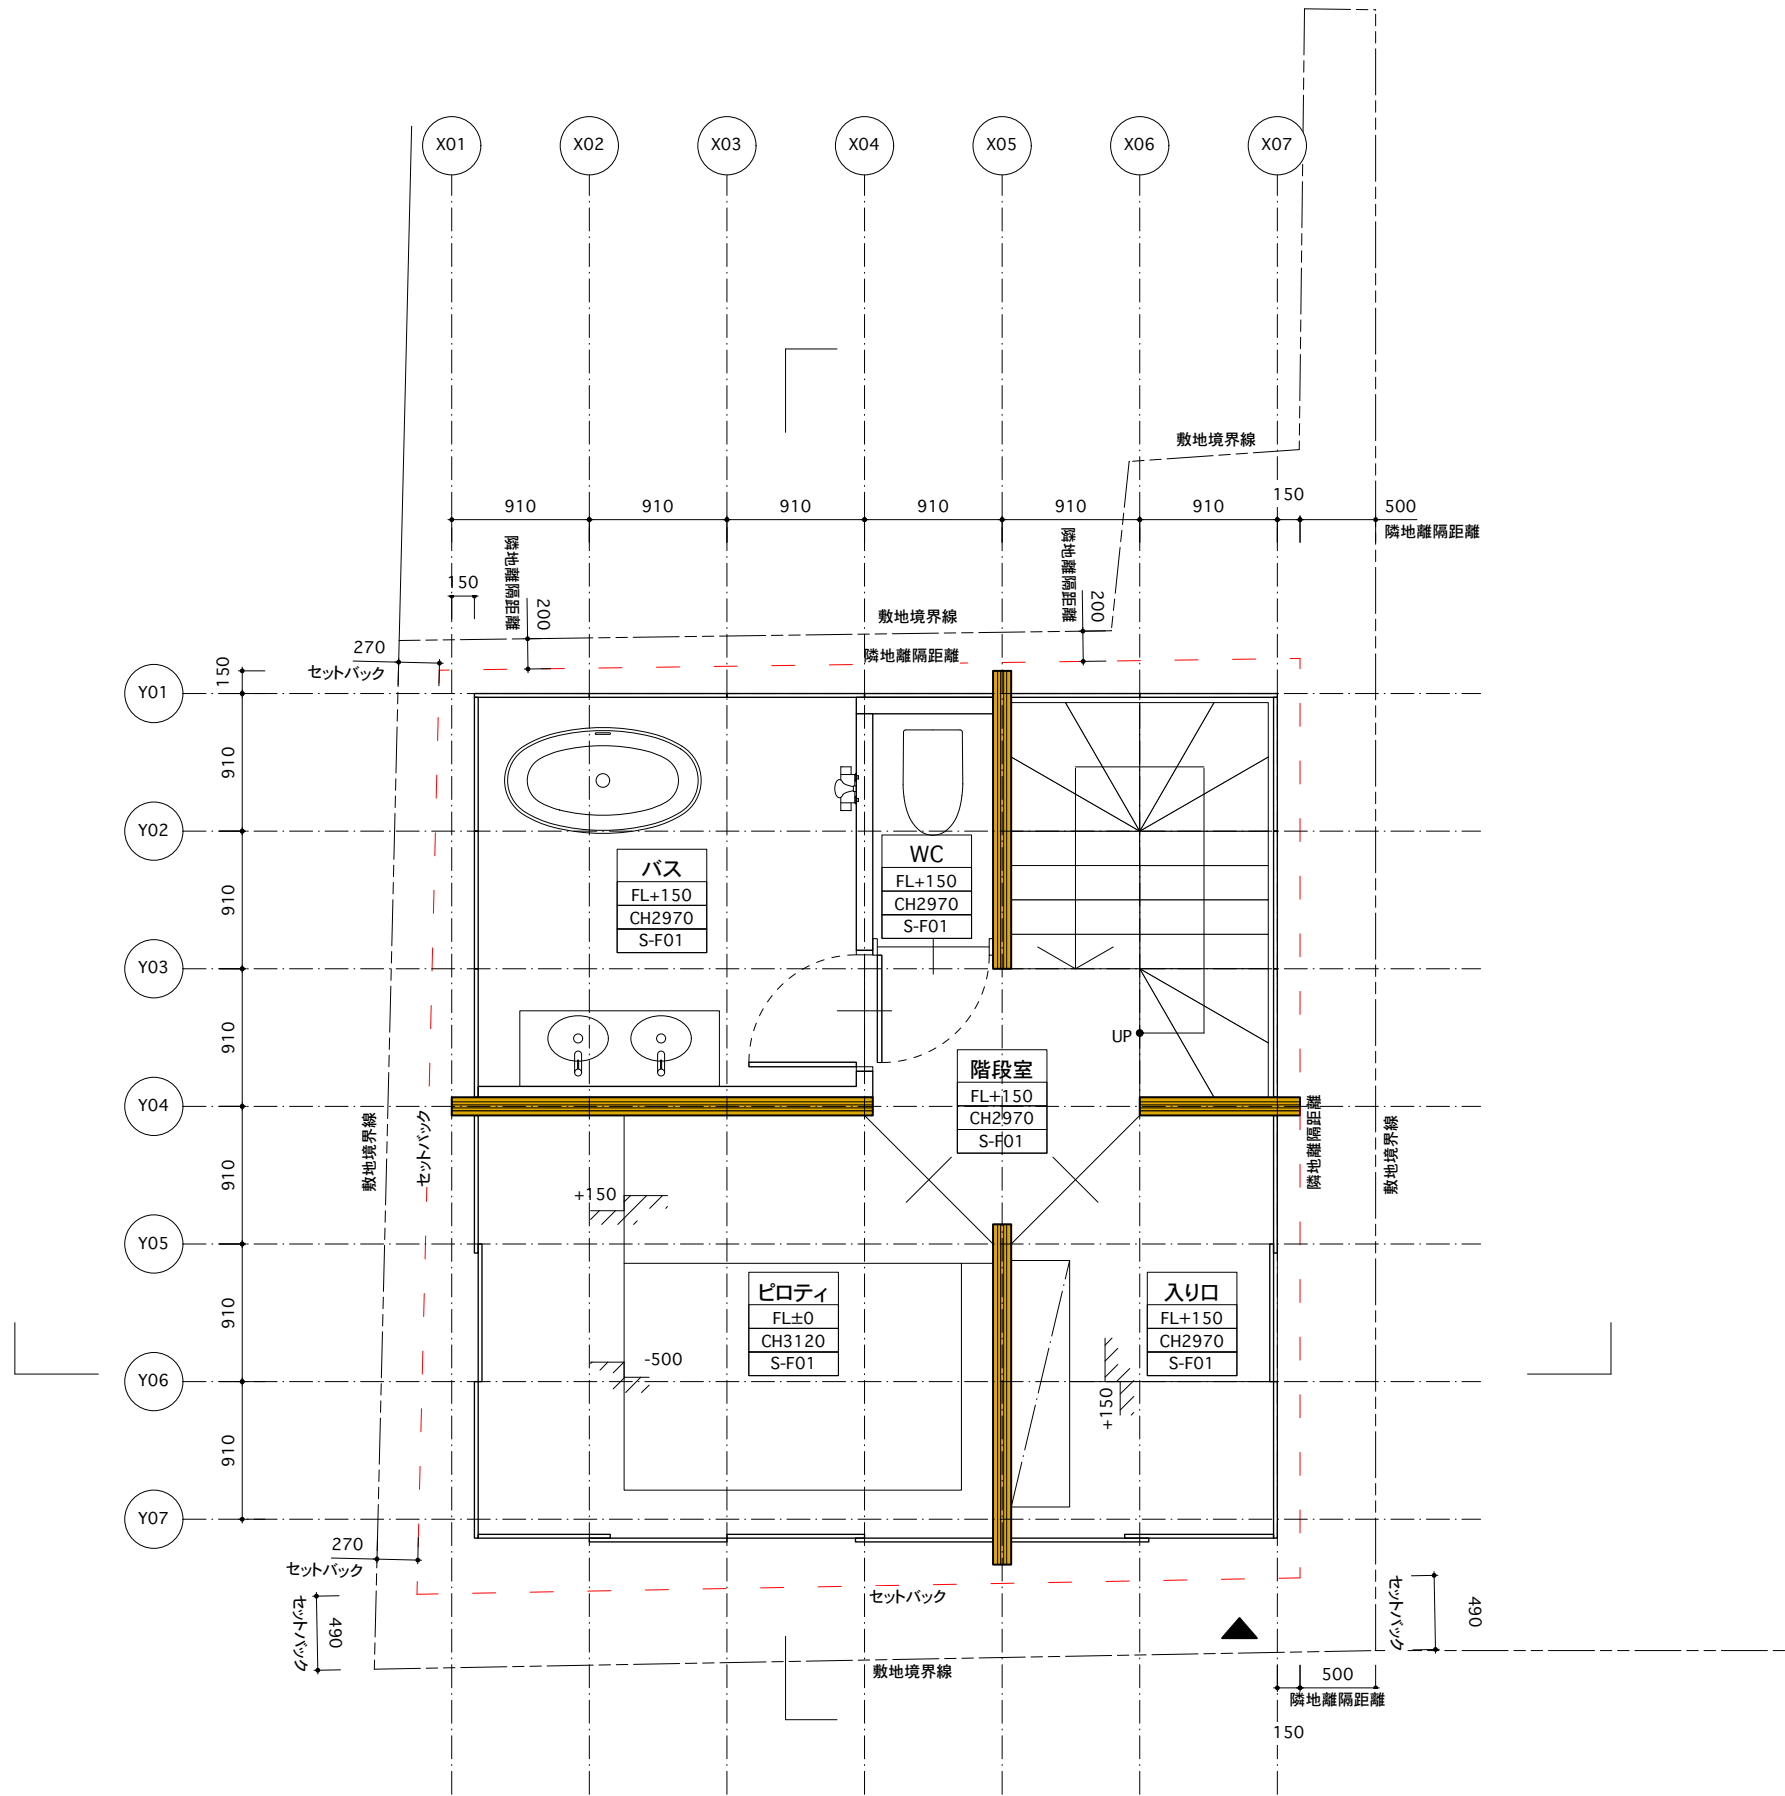

1F=33.52m²
2F=33.52m²
3F=23.77m²
合計=90.81



staple studio

〒103-0024
東京都中央区日本橋小舟町14-7
SOIL Nihonbashi 402

第369584号
管理建築士 / 一級建築士
黒木涼

凡例

title

1f平面図

scale

1:50

drawn by

no.

a-02


project

(仮) hyotan

date


2026/04/21

checked by

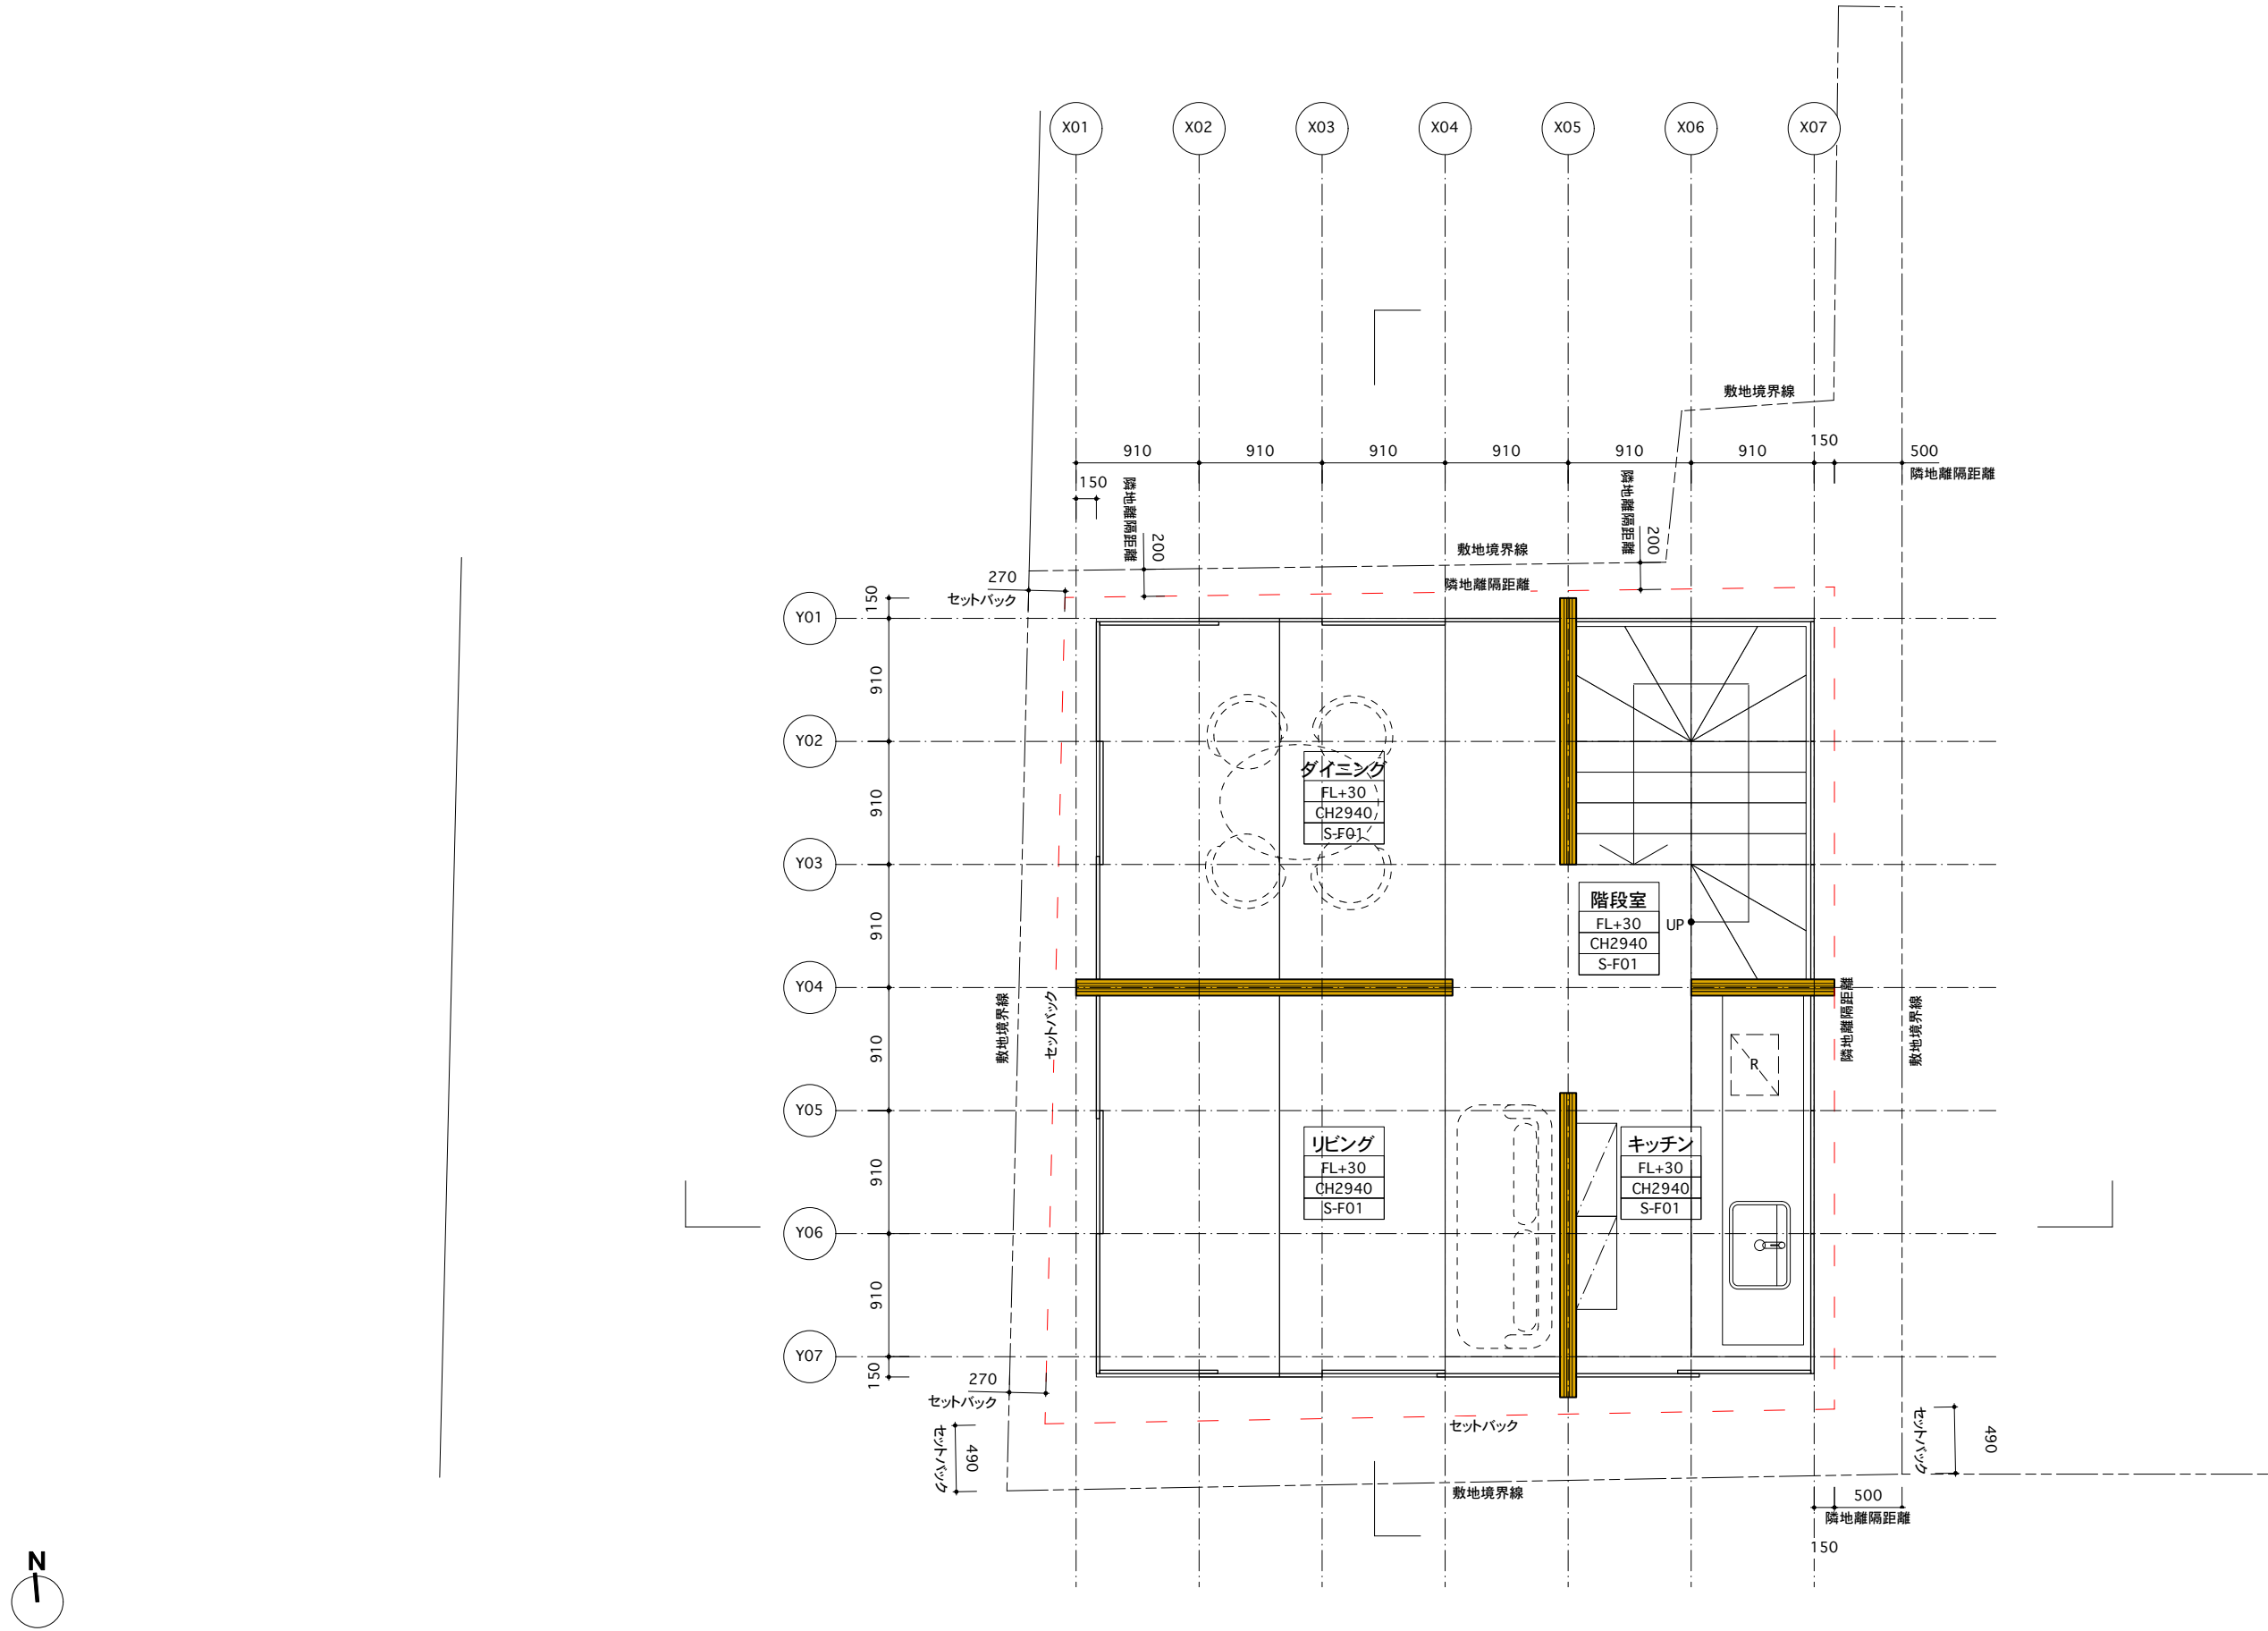

staple studio

〒103-0024 東京都中央区日本橋小舟町14-7 SOIL Nihonbashi 402	凡例						title	scale	drawn by	no. a-03
							2f平面図	1:50		
							project	date	checked by	
	第369584号 管理建築士 / 一級建築士 黒木涼						(仮) hyotan	2026/04/21		

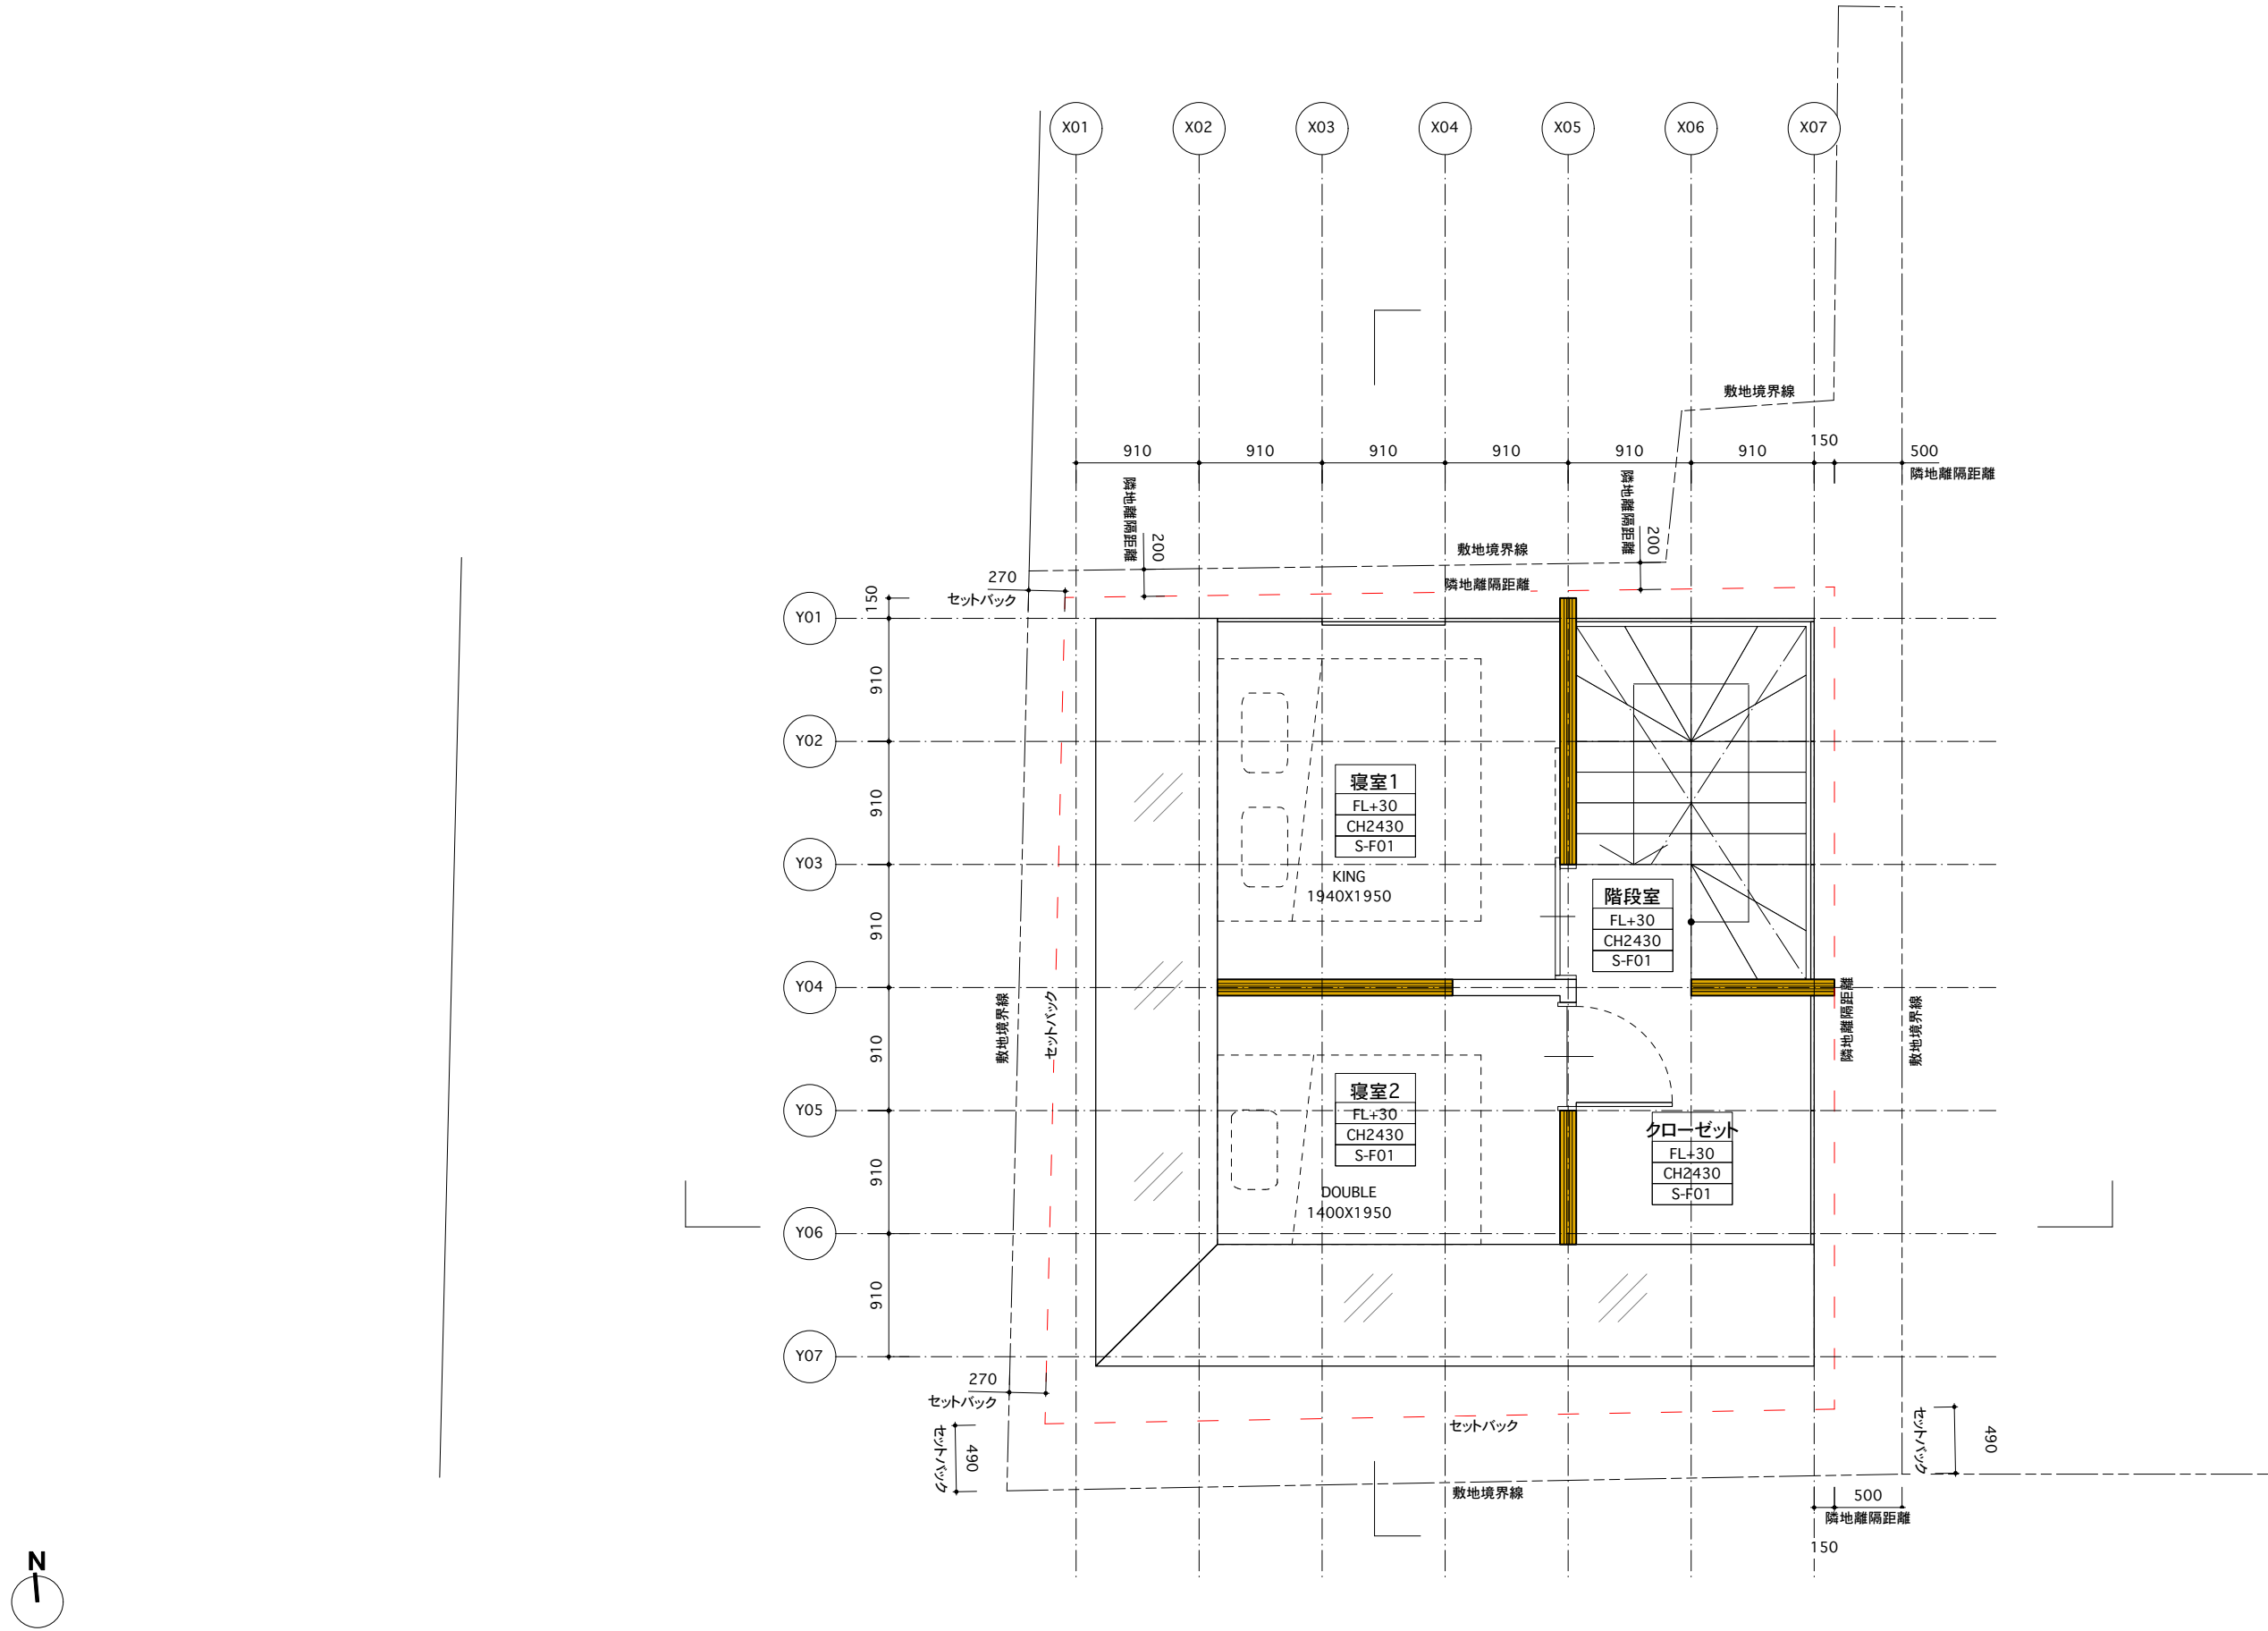

staple studio

〒103-0024 東京都中央区日本橋小舟町14-7 SOIL Nihonbashi 402	凡例					title		scale	drawn by	no. a-04
						3f平面図		1:50		
						project		date	checked by	
	第369584号 管理建築士 / 一級建築士 黒木涼					(仮) hyotan		2026/04/21		





staple studio


〒103-0024
東京都中央区日本橋小舟町14-7
SOIL Nihonbashi 402

第369584号
管理建築士 / 一級建築士
黒木涼

凡例							title	scale	drawn by	no. a-05
							rf平面図	1:50		
							project (仮) hyotan	date 2026/04/21	checked by	

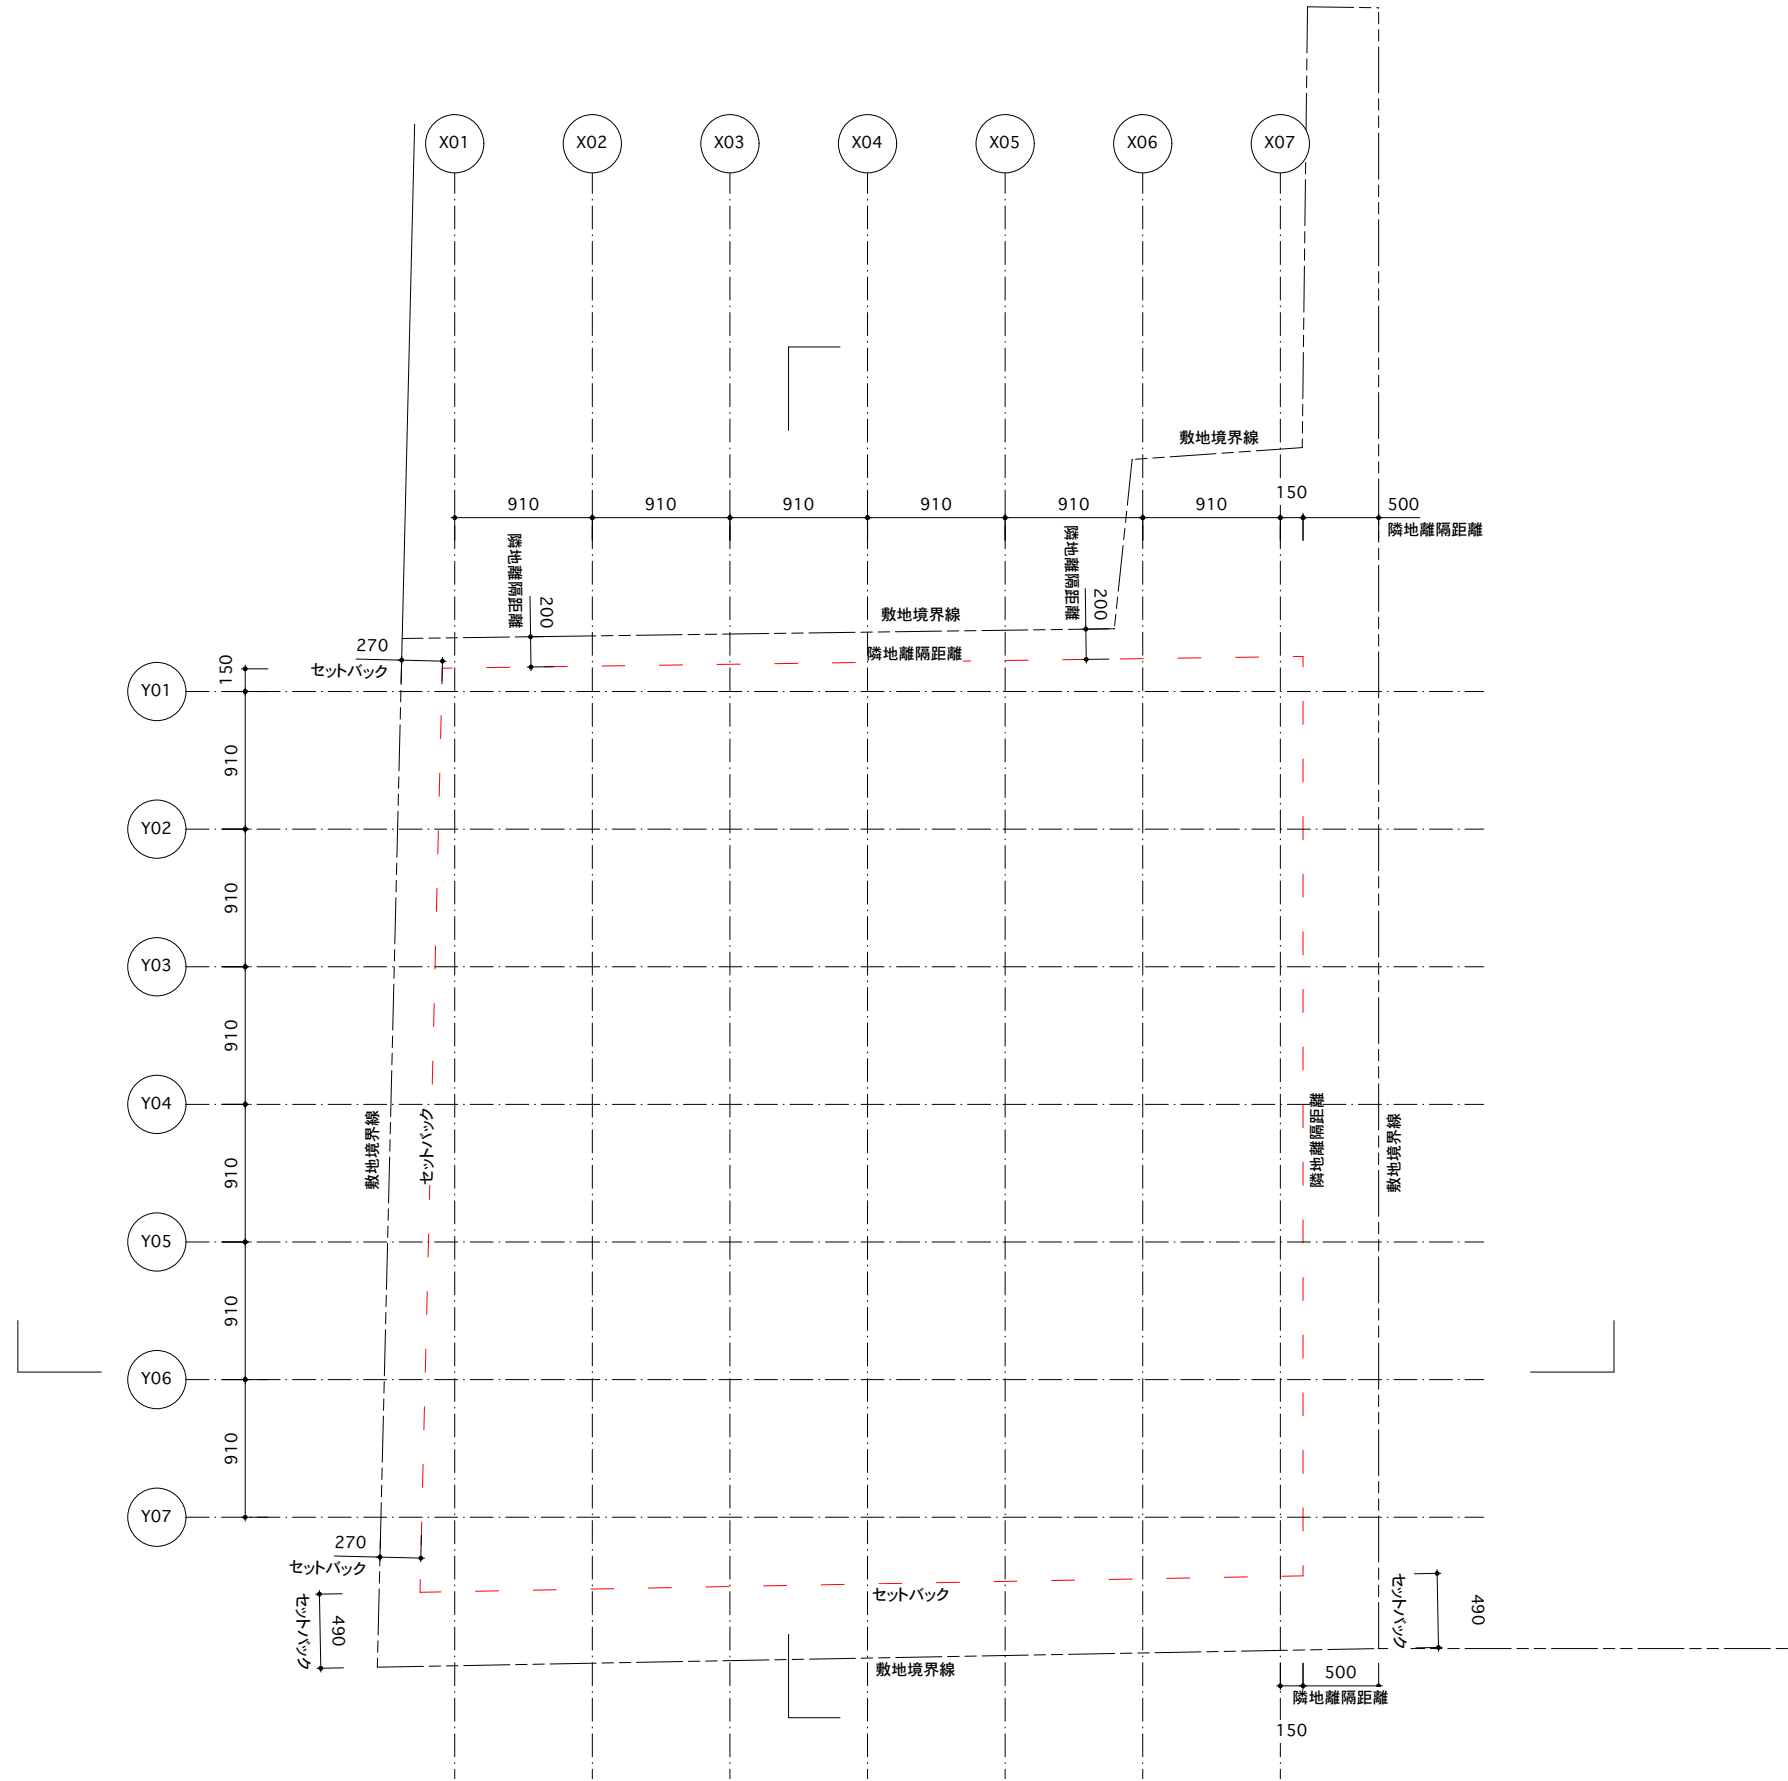

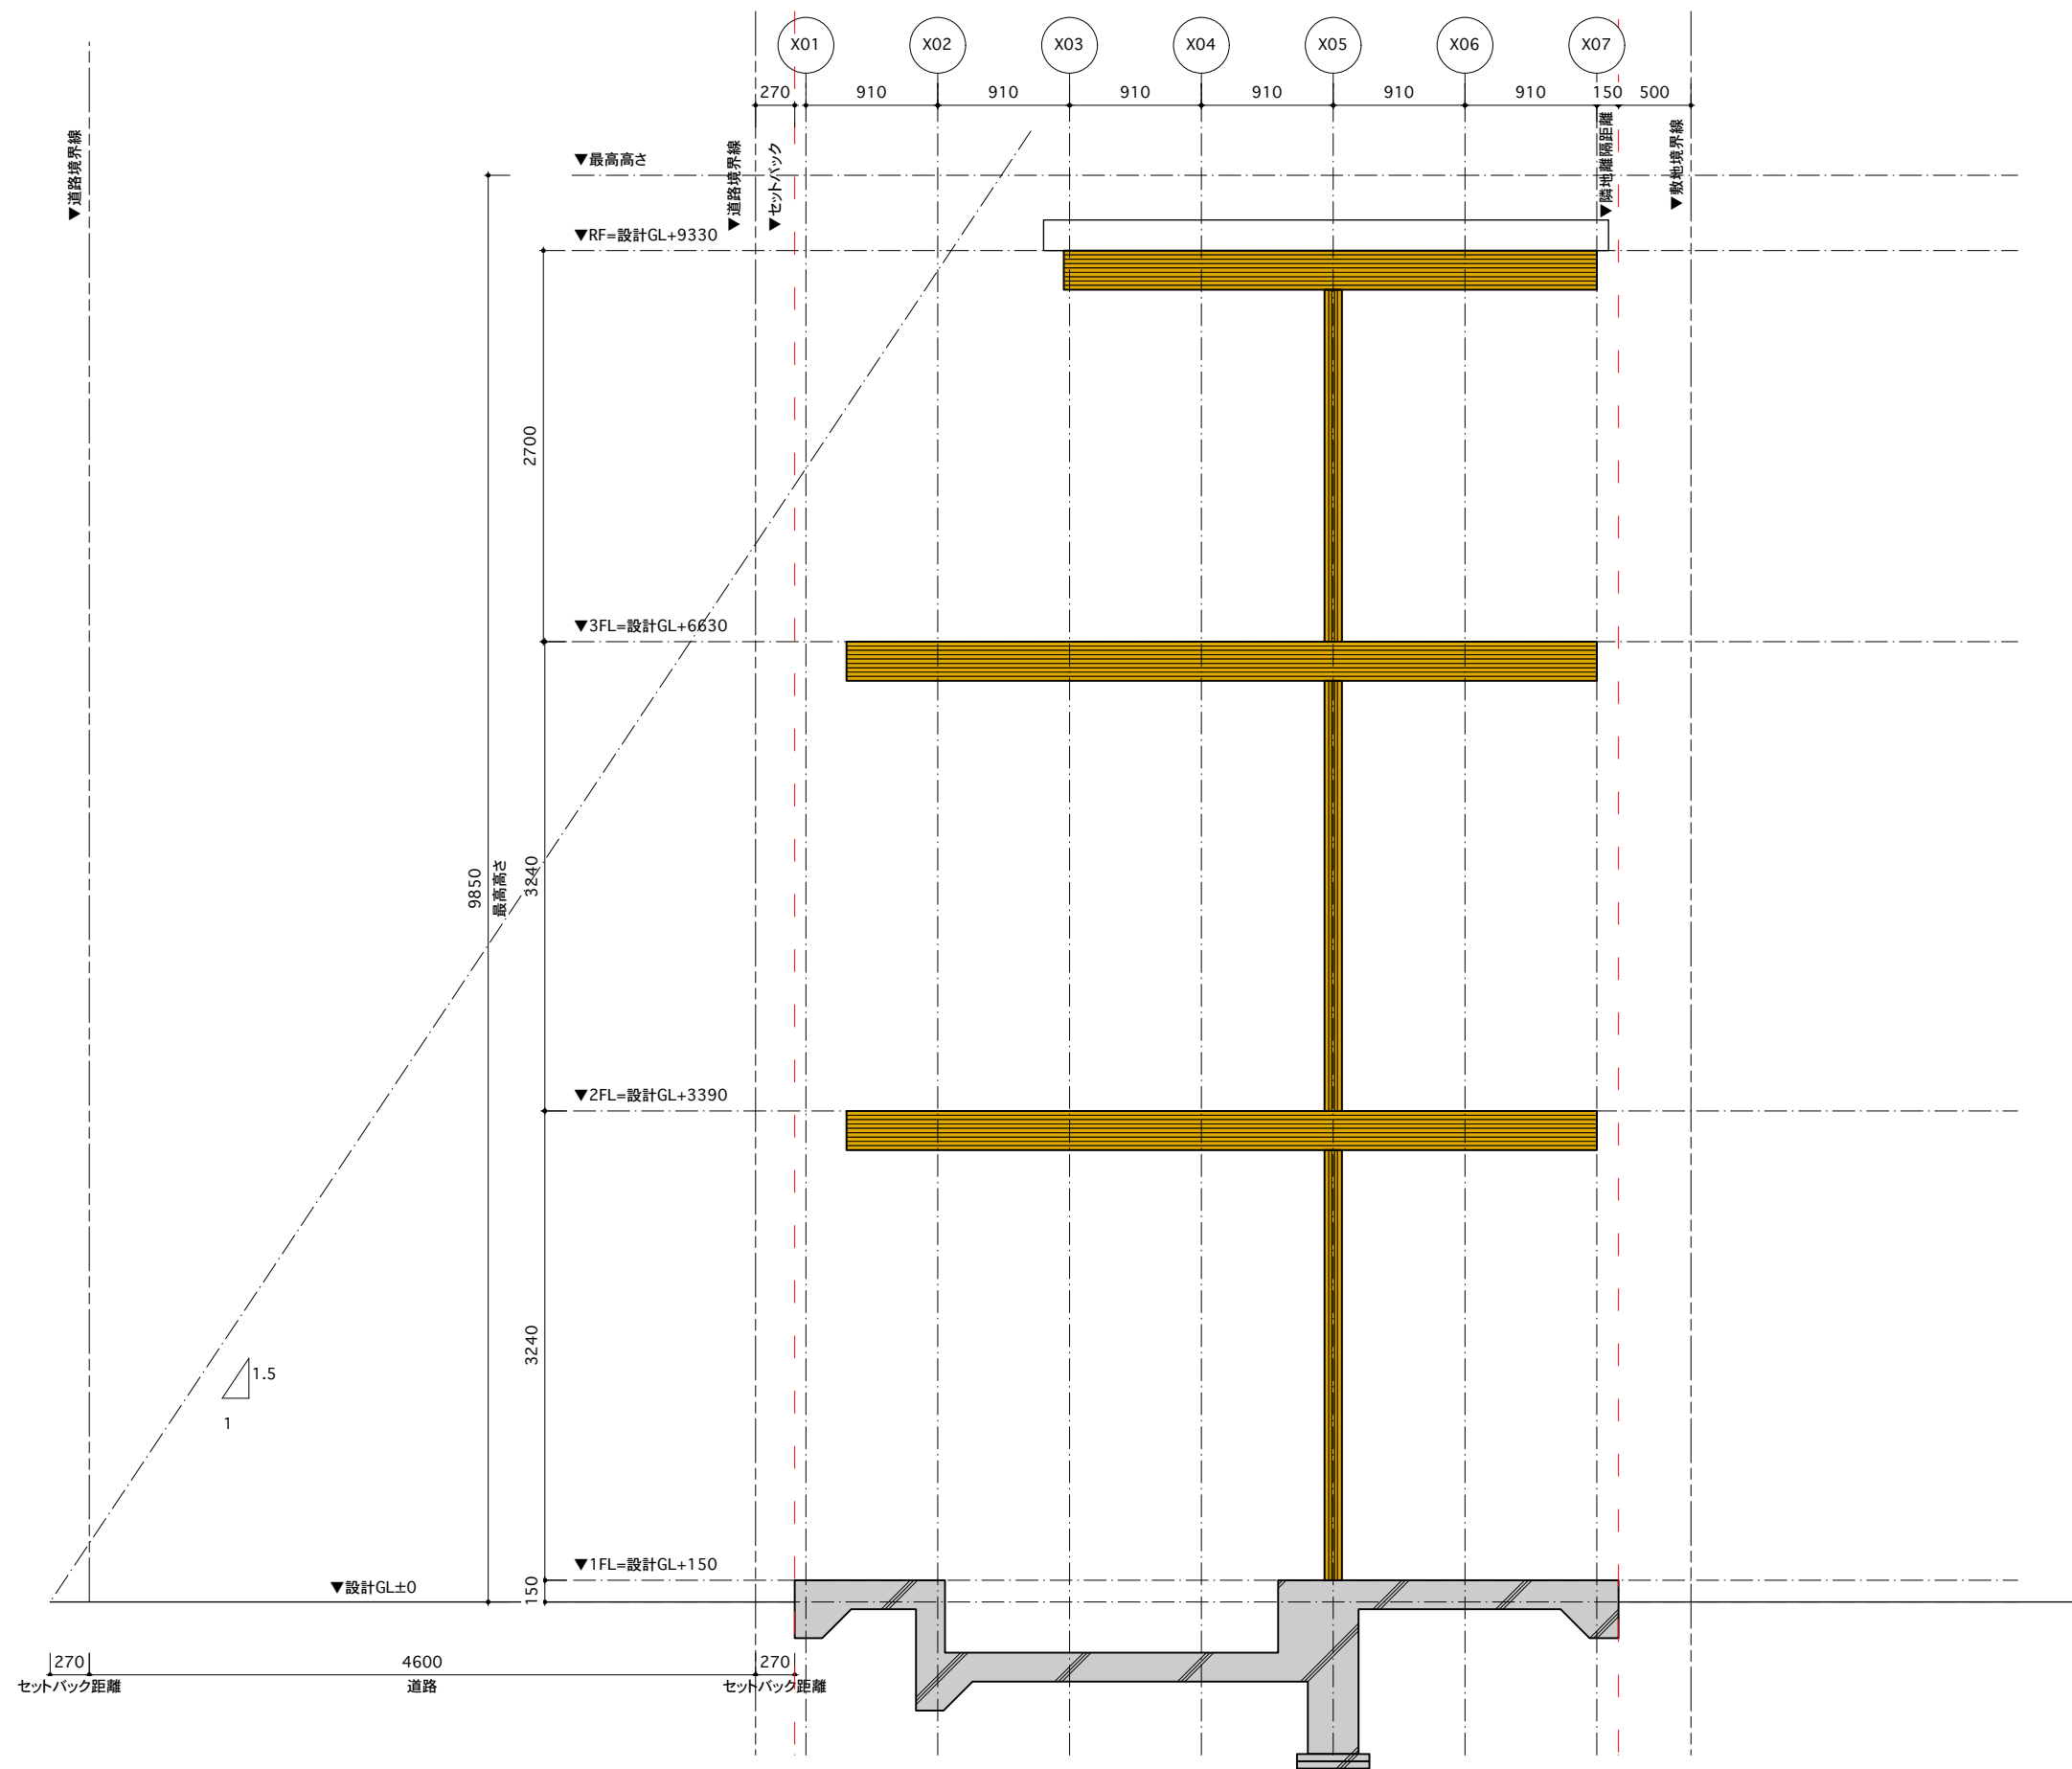

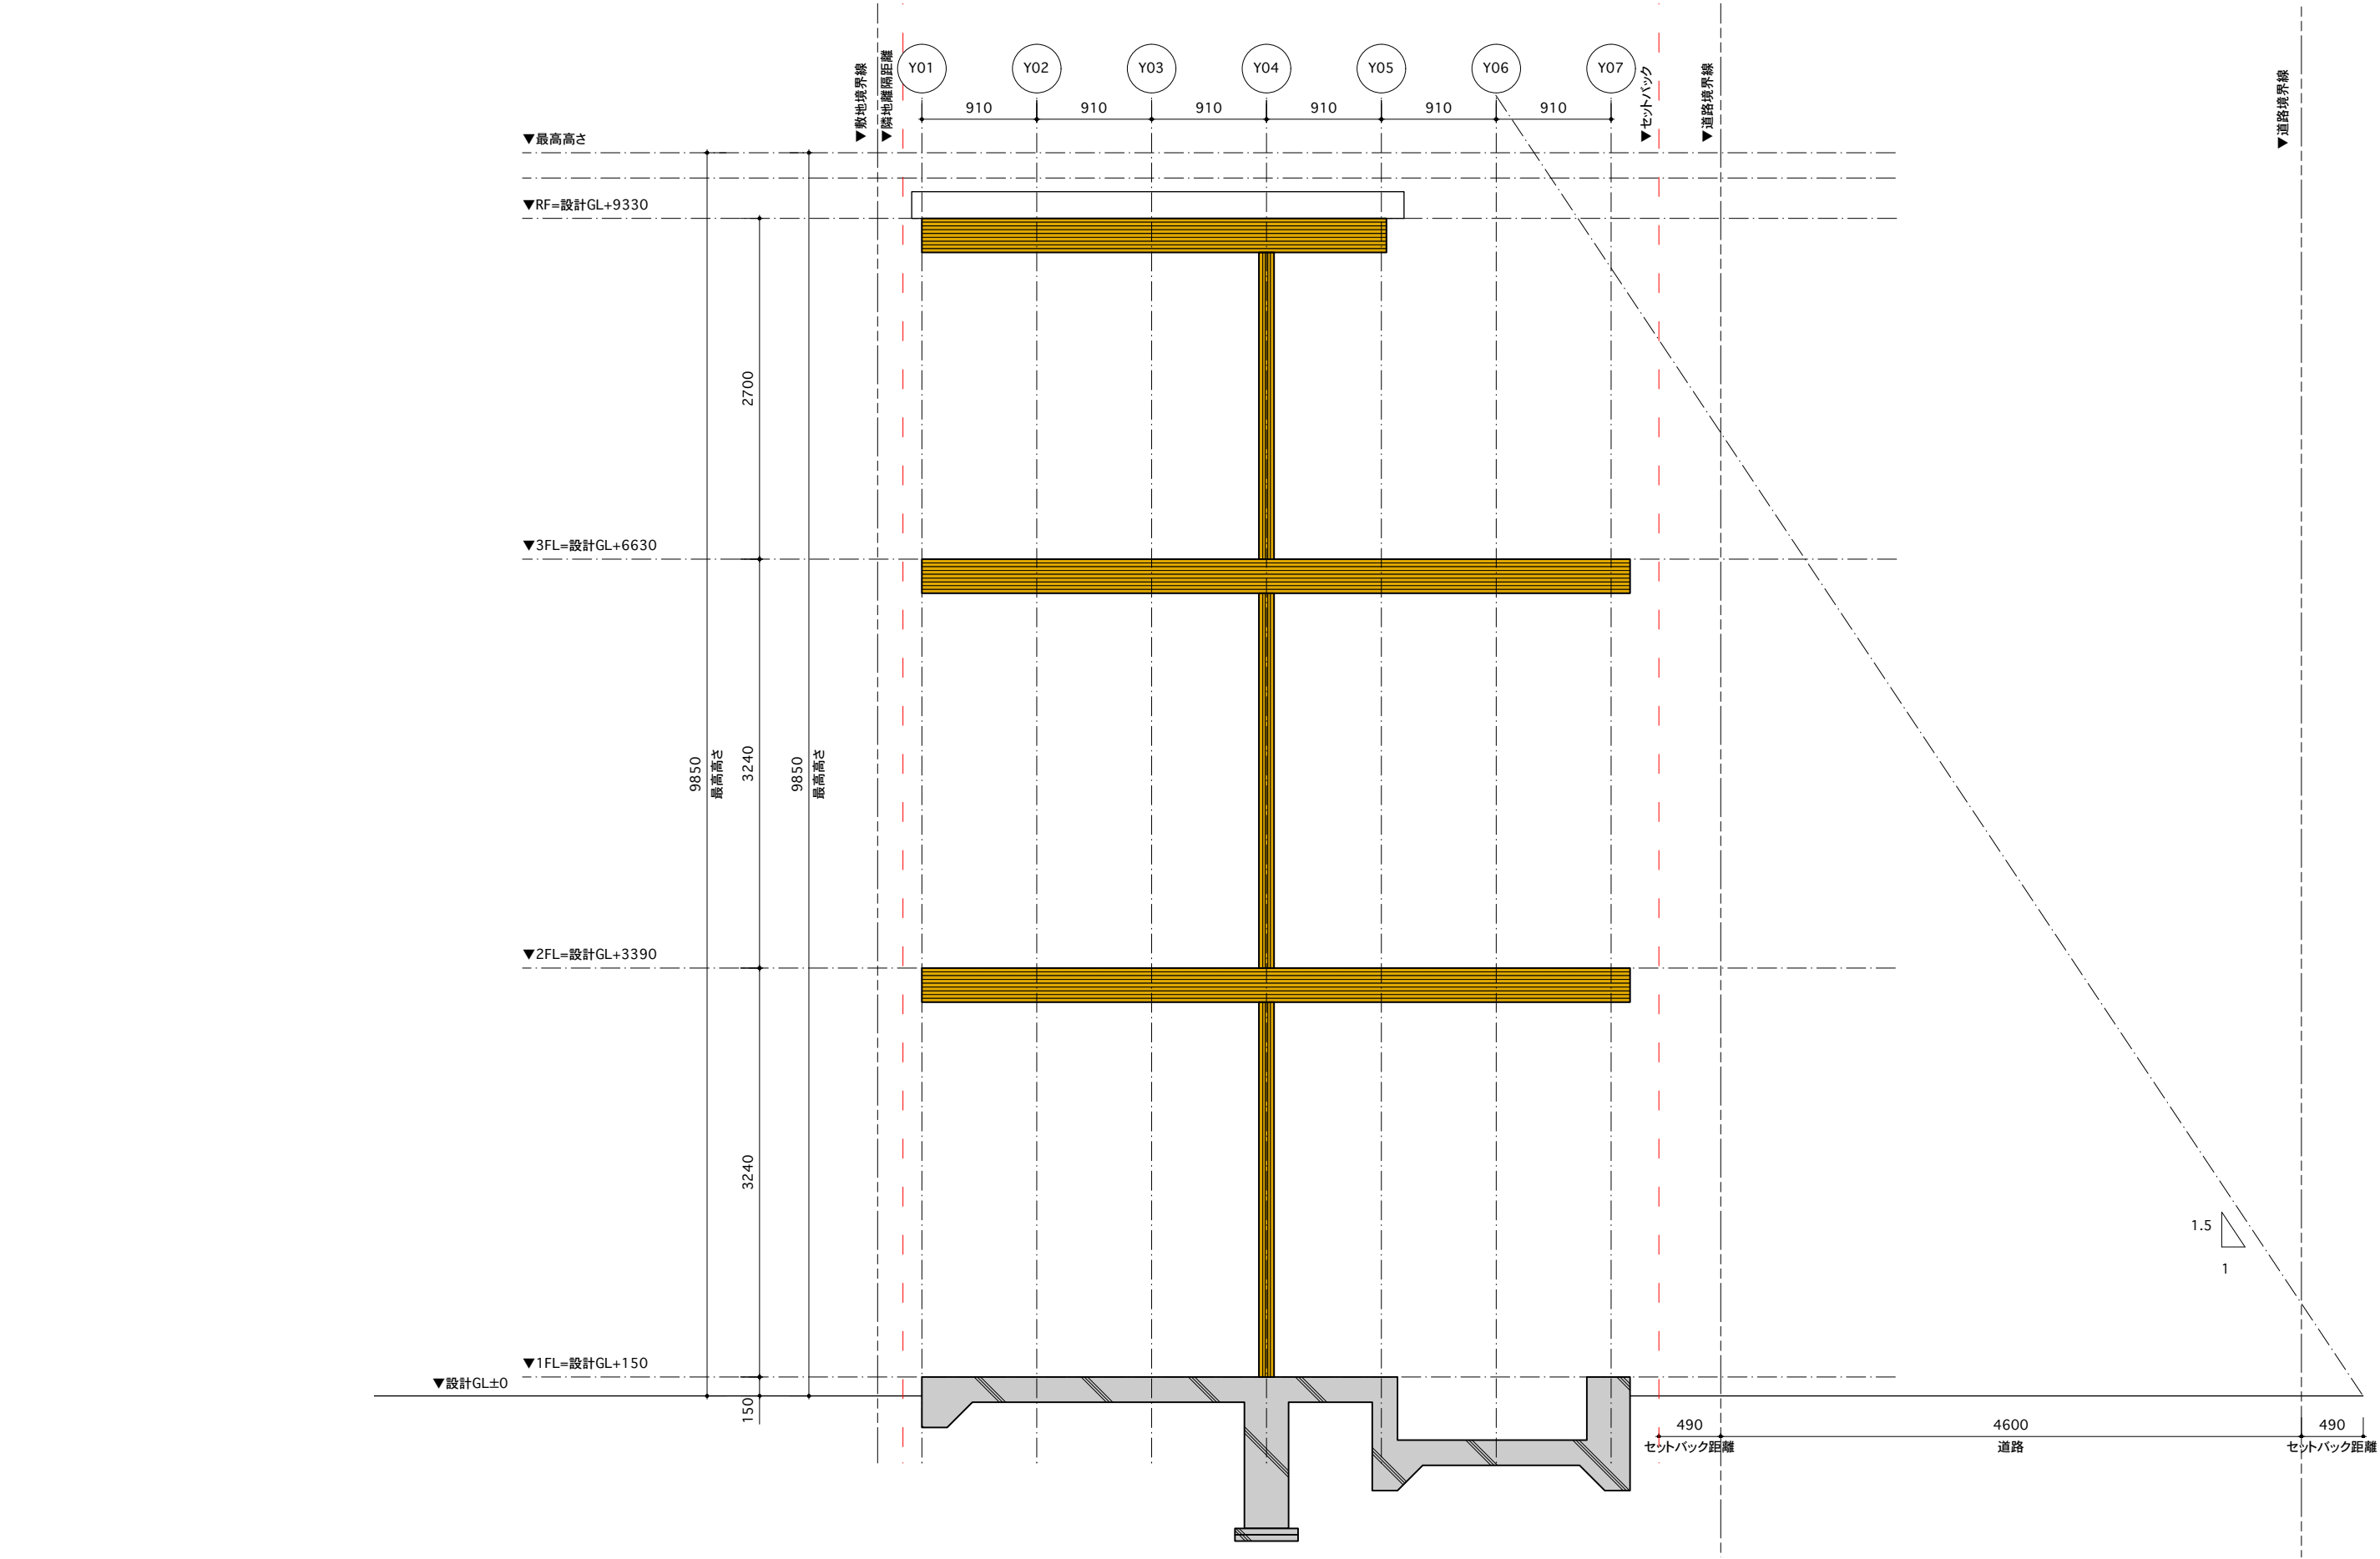

staple studio	〒103-0024 東京都中央区日本橋小舟町14-7 SOIL Nihonbashi 402	凡例						title	scale	drawn by	no.
								東西断面図	1:50		a-07
								project	date	checked by	
								(仮) hyotan	2026/04/21		
	第369584号 管理建築士 / 一級建築士 黒木涼										